


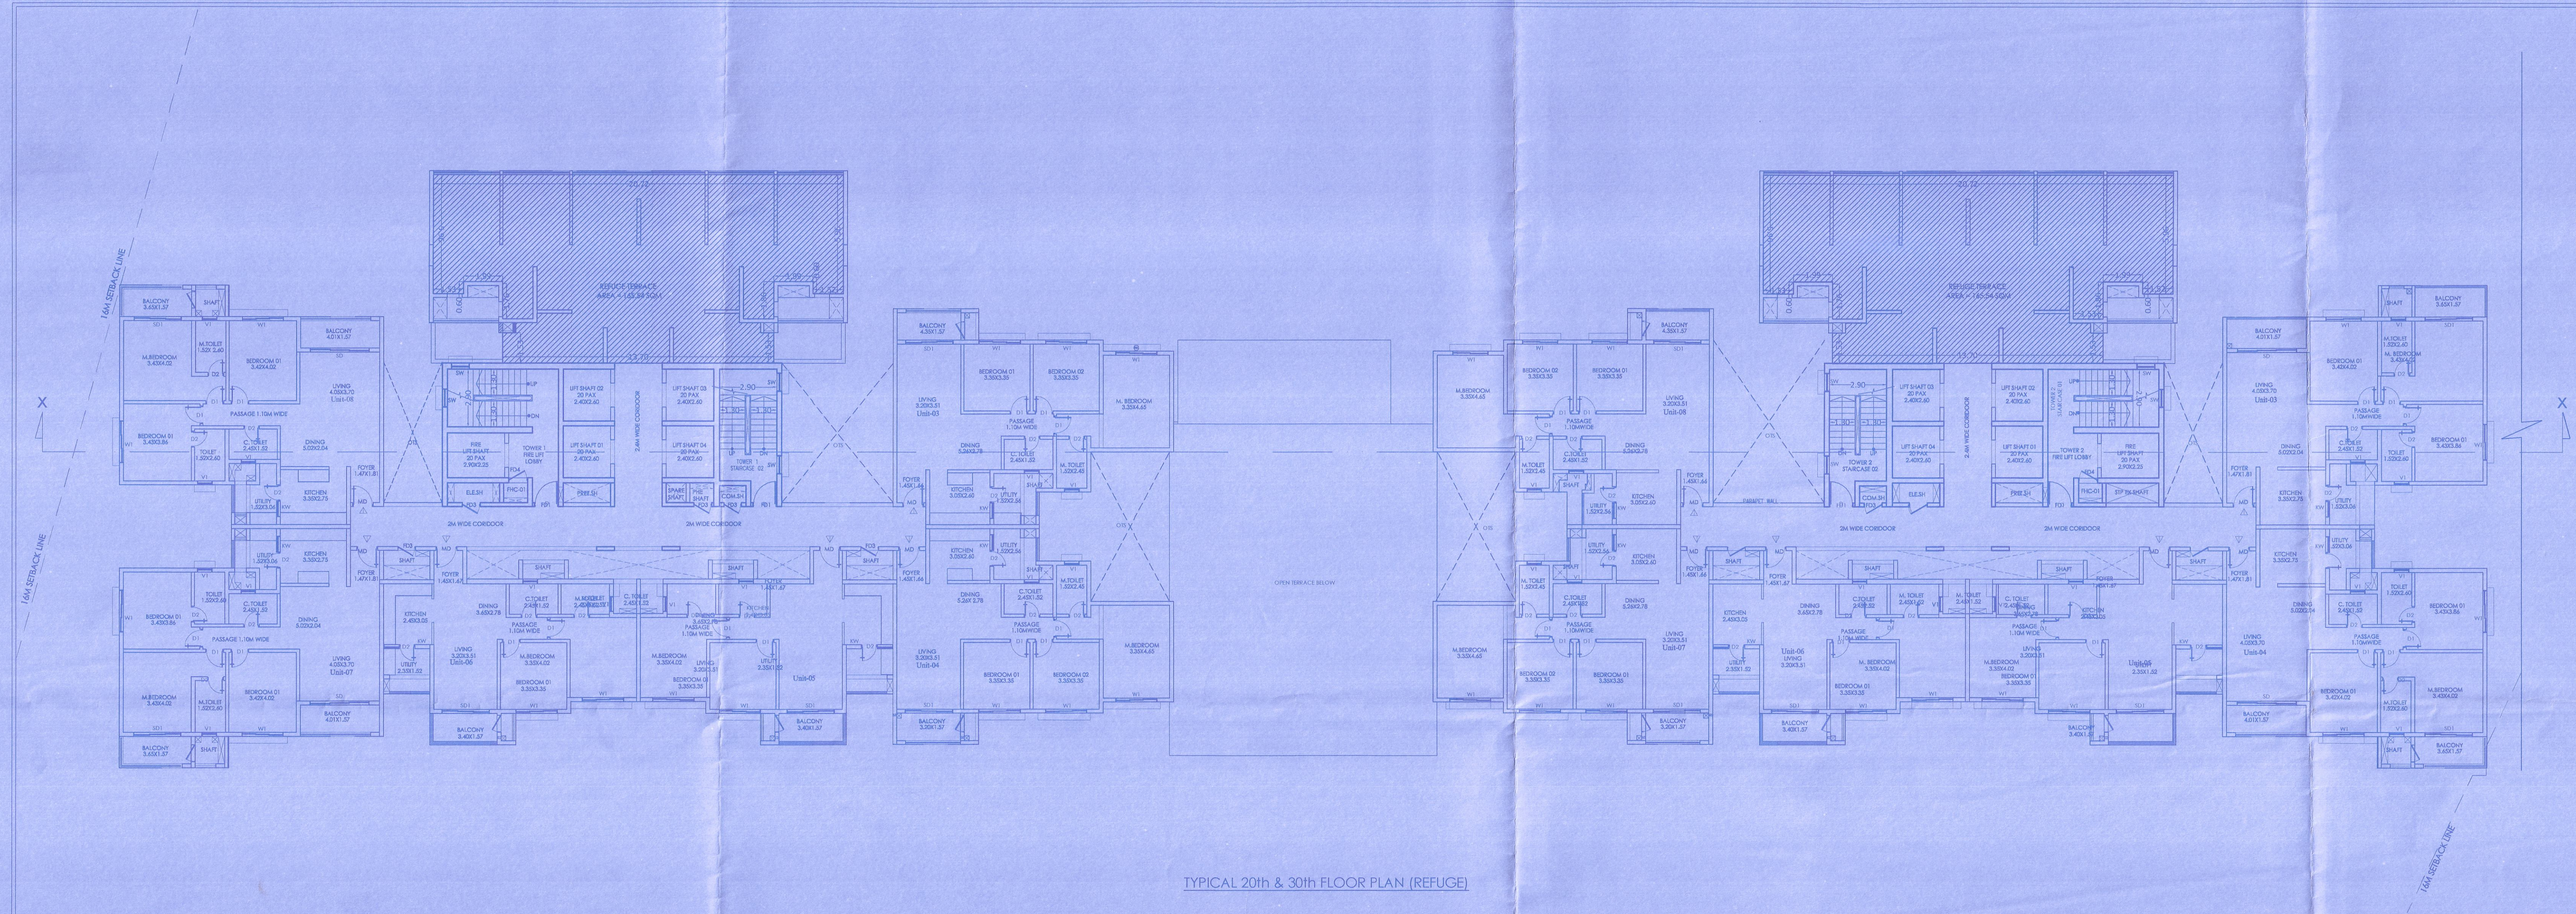

TYPICAL 20th & 30th FLOOR PLAN (REFUGE)

SANCTIONING AUTHORITY:-

ಇದರಲ್ಲಿರುವ ಸ್ಥಳೀಯ ಸರ್ಕಾರದ
2026-27 ರಿಂದ 09 JUL 2026
ಸಂಪನ್ಮೂಲ ಸಚಿವರ ಕಛೇರಿ
ಬೆಂಗಳೂರು ನಗರ ಸರ್ಕಾರ
ಬೆಂಗಳೂರು

BUILT UP AREA STATEMENT TOWER A + TOWER B RECREATIONAL BUILDING + BASEMENT FLOOR														
AREA STATEMENT IN SQM														
FLOOR	GROSS AREA	PRODUCTION FOR DUCTS & DTY	DEDUCTIONS FOR GARDEN & DOUBLE HT	BUILT UP AREA	PARKING	NON FAR AREA	STAIRCASE	REFUGE AREA	TOTAL NON FAR AREA	FAR AREA	NO'S OF UNIT			
	A	B	C	D	E	F	G	H	I	J	K	L	M	N
BASEMENT -1	781.18	28.56	---	781.22	7100.15	62.84	---	---	7103.08	242.13	---	---	---	---
BASEMENT -2	781.18	28.56	---	781.22	7100.15	62.84	---	---	7103.08	242.13	---	---	---	---
BASEMENT -3	781.18	28.56	---	781.22	7100.15	62.84	---	---	7103.08	242.13	---	---	---	---
GROUND	2783.49	158.41	158.41	2412.04	3232.75	81.12	---	---	3232.75	110.85	18	---	---	---
1st FLOOR	2815.29	158.42	151.92	2777.85	---	81.12	---	---	81.12	2281.83	18	---	---	---
2nd FLOOR	2783.47	158.42	151.92	2684.13	---	81.12	---	---	81.12	2281.83	18	---	---	---
3rd FLOOR	2783.47	158.42	151.92	2684.13	---	81.12	---	---	81.12	2281.83	18	---	---	---
4th FLOOR	2783.47	158.42	151.92	2684.13	---	81.12	---	---	81.12	2281.83	18	---	---	---
5th FLOOR	2783.47	158.42	151.92	2684.13	---	81.12	---	---	81.12	2281.83	18	---	---	---
6th FLOOR	2783.47	158.42	151.92	2684.13	---	81.12	---	---	81.12	2281.83	18	---	---	---
7th FLOOR	2783.47	158.42	151.92	2684.13	---	81.12	---	---	81.12	2281.83	18	---	---	---
8th FLOOR	2783.47	158.42	151.92	2684.13	---	81.12	---	---	81.12	2281.83	18	---	---	---
9th FLOOR	2783.47	158.42	151.92	2684.13	---	81.12	---	---	81.12	2281.83	18	---	---	---
10th FLOOR	2783.47	158.42	151.92	2684.13	---	81.12	---	---	81.12	2281.83	18	---	---	---
11th FLOOR	2783.47	158.42	151.92	2684.13	---	81.12	---	---	81.12	2281.83	18	---	---	---
12th FLOOR	2783.47	158.42	151.92	2684.13	---	81.12	---	---	81.12	2281.83	18	---	---	---
13th FLOOR	2783.47	158.42	151.92	2684.13	---	81.12	---	---	81.12	2281.83	18	---	---	---
14th FLOOR	2783.47	158.42	151.92	2684.13	---	81.12	---	---	81.12	2281.83	18	---	---	---
15th FLOOR	2783.47	158.42	151.92	2684.13	---	81.12	---	---	81.12	2281.83	18	---	---	---
16th FLOOR	2783.47	158.42	151.92	2684.13	---	81.12	---	---	81.12	2281.83	18	---	---	---
17th FLOOR	2783.47	158.42	151.92	2684.13	---	81.12	---	---	81.12	2281.83	18	---	---	---
18th FLOOR	2783.47	158.42	151.92	2684.13	---	81.12	---	---	81.12	2281.83	18	---	---	---
19th FLOOR	2783.47	158.42	151.92	2684.13	---	81.12	---	---	81.12	2281.83	18	---	---	---
20th FLOOR	2783.47	158.42	151.92	2684.13	---	81.12	---	---	81.12	2281.83	18	---	---	---
21st FLOOR	2783.47	158.42	151.92	2684.13	---	81.12	---	---	81.12	2281.83	18	---	---	---
22nd FLOOR	2783.47	158.42	151.92	2684.13	---	81.12	---	---	81.12	2281.83	18	---	---	---
23rd FLOOR	2783.47	158.42	151.92	2684.13	---	81.12	---	---	81.12	2281.83	18	---	---	---
24th FLOOR	2783.47	158.42	151.92	2684.13	---	81.12	---	---	81.12	2281.83	18	---	---	---
25th FLOOR	2783.47	158.42	151.92	2684.13	---	81.12	---	---	81.12	2281.83	18	---	---	---
26th FLOOR	2783.47	158.42	151.92	2684.13	---	81.12	---	---	81.12	2281.83	18	---	---	---
27th FLOOR	2783.47	158.42	151.92	2684.13	---	81.12	---	---	81.12	2281.83	18	---	---	---
28th FLOOR	2783.47	158.42	151.92	2684.13	---	81.12	---	---	81.12	2281.83	18	---	---	---
29th FLOOR	2783.47	158.42	151.92	2684.13	---	81.12	---	---	81.12	2281.83	18	---	---	---
30th FLOOR	2783.47	158.42	151.92	2684.13	---	81.12	---	---	81.12	2281.83	18	---	---	---
TERACE	311.85	---	---	311.85	---	---	---	---	311.85	662.16	27224.53	08833.19	534	---
TOTAL	104849.75	7185.53	525.10	98052.12	23123.18	2627.38	911.81	662.16	27224.53	08833.19	534	---	---	---

FAR CALCULATIONS:

FAR = $\frac{\text{TOTAL FAR AREA}}{\text{SITE AREA - CA}}$

FAR = $\frac{69833.59 \text{ Sqm}}{32677.91-1638.00 \text{ Sqm}} = 2.249 < 2.25$

GROUND COVERAGE:

COVERAGE = $\frac{\text{GF AREA+SWIMMING POOL}}{\text{SITE AREA-CA-ROAD}} \times 100$

COVERAGE = $\frac{2904.43+598.14}{32677.91-1638-11307.55 \text{ Sqm}} = 17.75\% < 55\%$

TOTAL BUILDING HEIGHT IS = 109.15 m & 14.60 m

NOTE : ALL DIMENSIONS ARE IN METER

SCALE - 1: 150

DWG No : 11 OF 13

DRAWINGS: TYPICAL 20th & 30th FLOOR PLAN (REFUGE)

TITLE :- PROPOSED RESIDENTIAL APARTMENT BUILDING PLAN IN SYNO:27/1, 27/3, 27/5, 27/8, 28/1 & 29/3, KATHA No : 27/1 3 5 8 28/1 29/3, PID No: 150200100100922059, OF KADA AGRAHARA VILLAGE, SARJAPURA HOBLI, ANEKAL TALUK, BANGALORE DIST.

OWNER:- Ms. DEBLEENA BANERJEE Mr. DARSHAN KANNAN M/s GODREJ PROPERTIES LTD

ENGINEER:- (PRAVEEN .B .V) Reg.No: BCC/BL-3.6 / E: 0099/2024-25