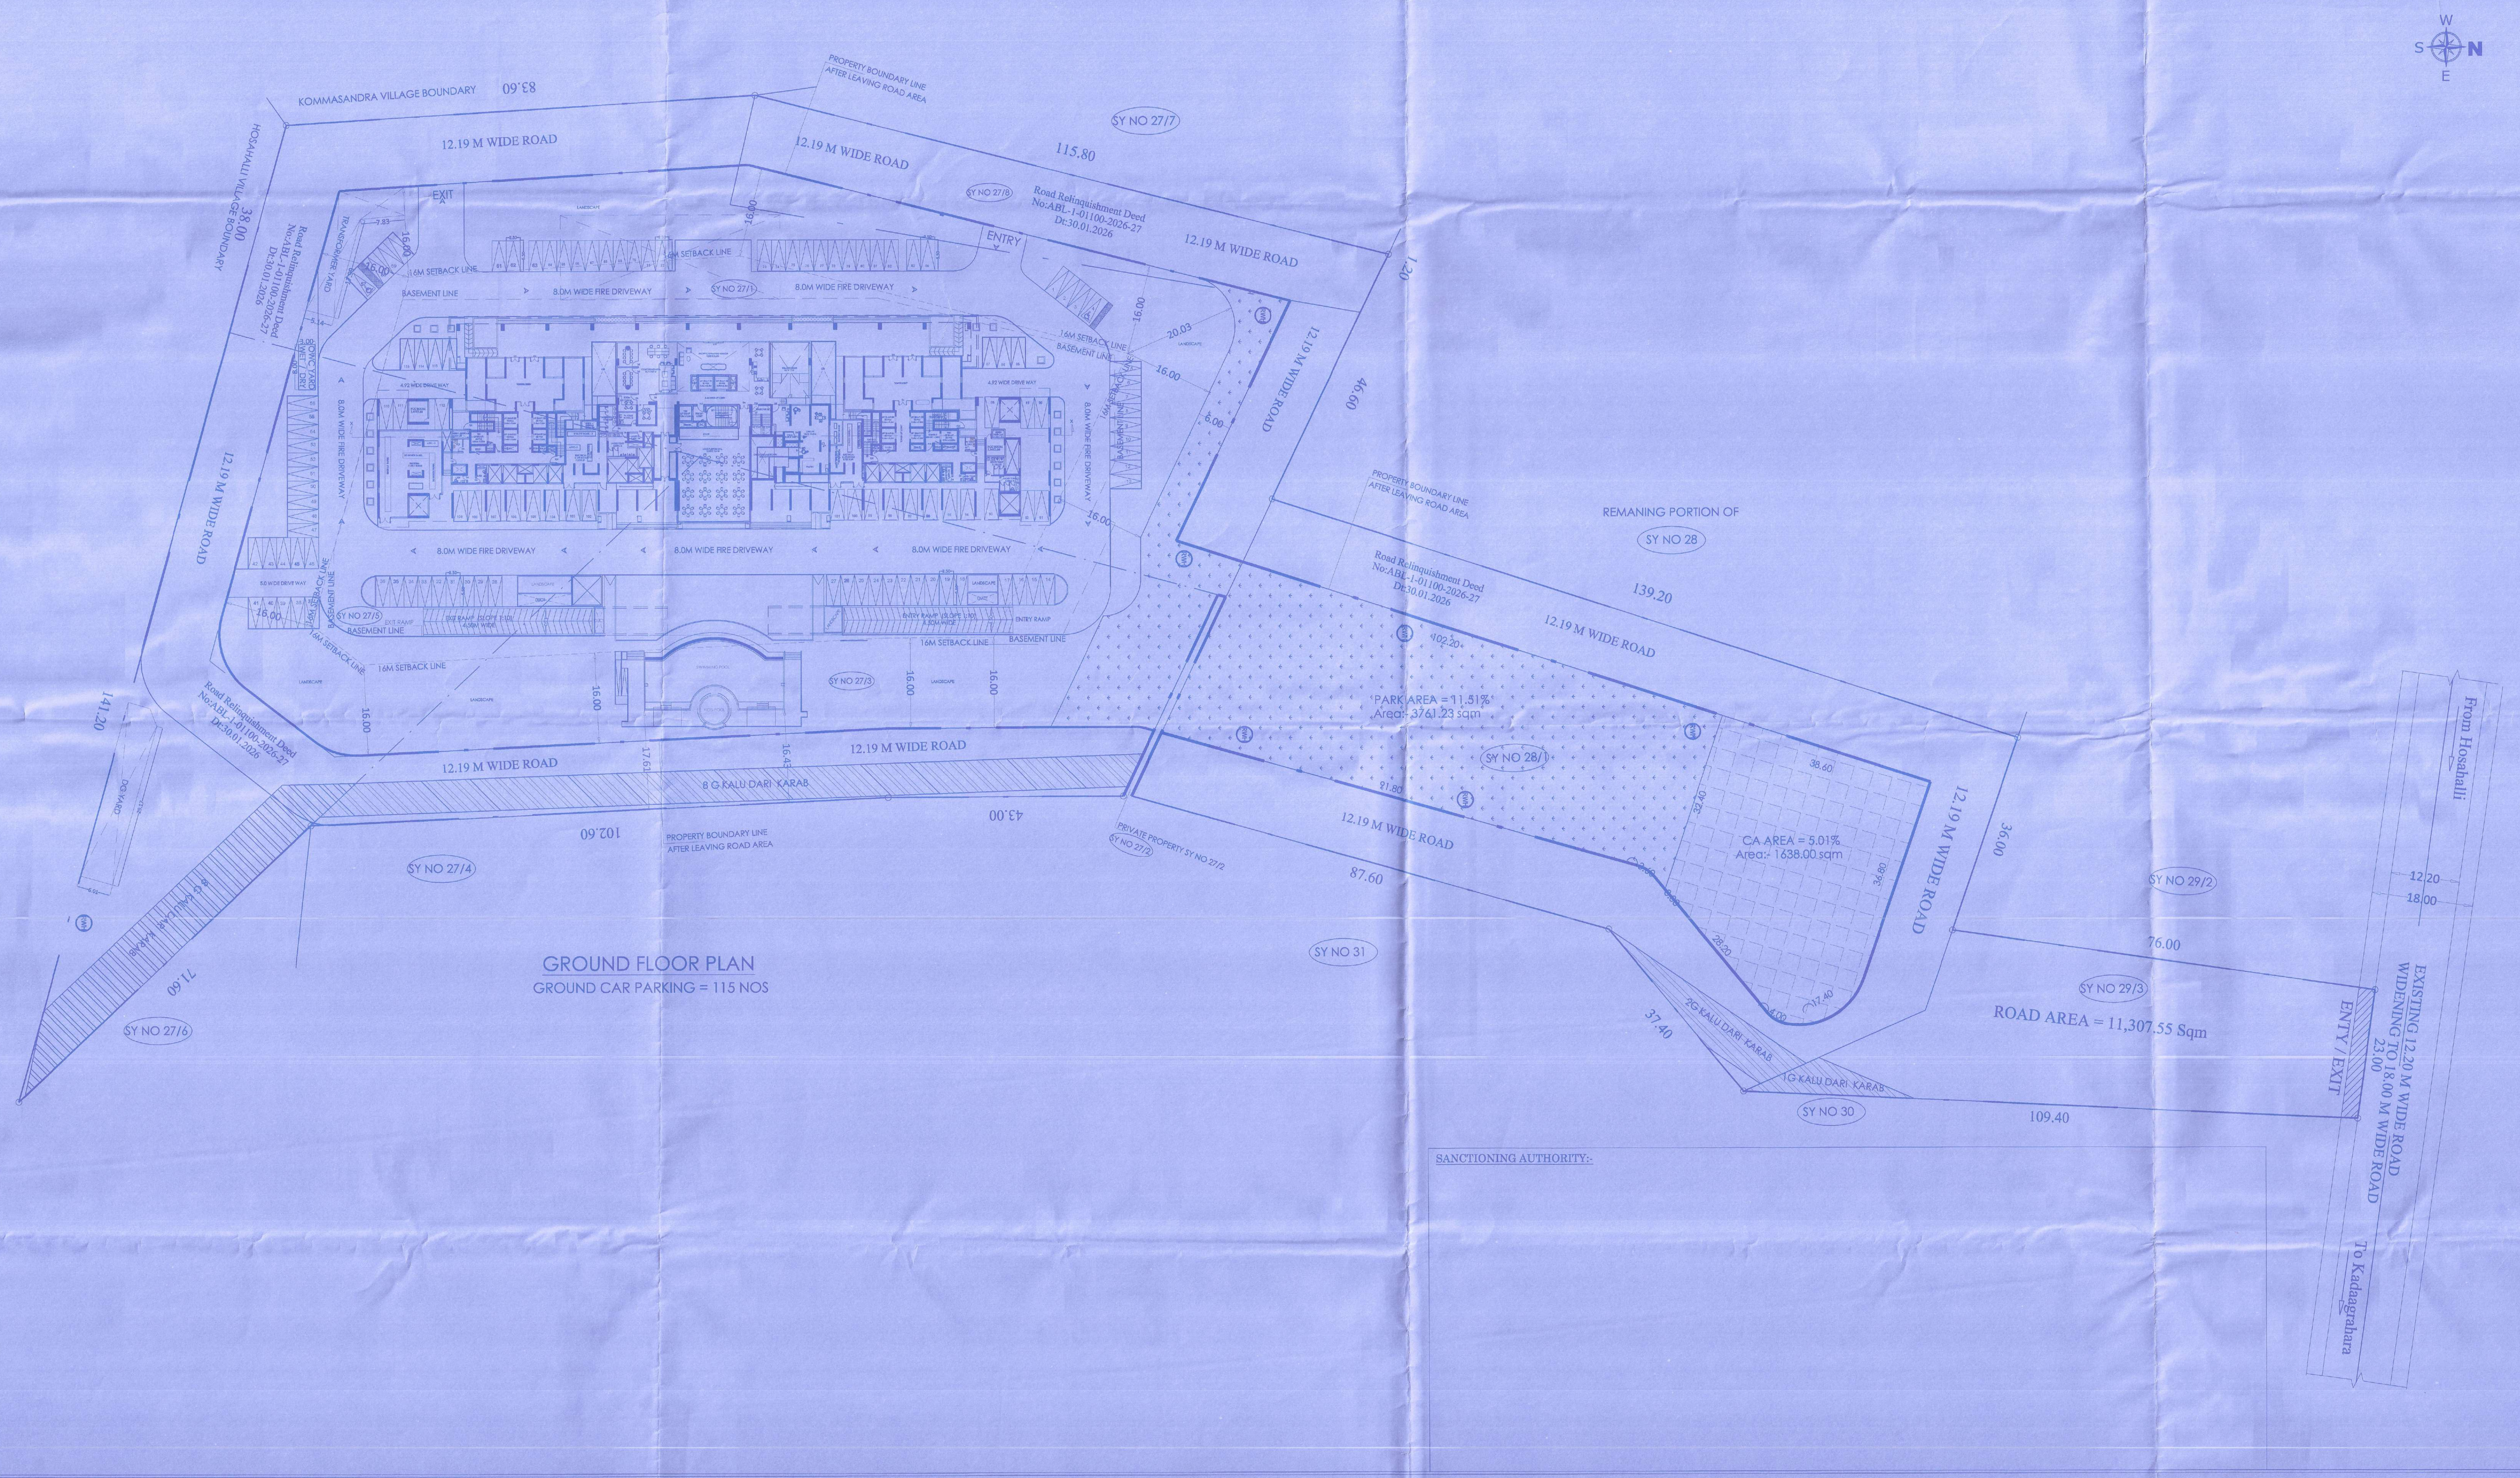

GROUND FLOOR PLAN

GROUND CAR PARKING = 115 NOS

SANCTIONING AUTHORITY:-

AREA STATEMENT								
SL.NO	VILLAGE	SY.NO	AREA IN		KARAB	BALANCE AREA		CONVERSION DETAILS
			ACRE	GUNTAS		ACRE	GUNTAS	
1	KADA AGRAHARA	27/1	2	13.08	-	2	13.08	ALN(A)(AS)SR:360/2012-13
2		27/3	1	22.08	8	1	14.08	AFF NO:301853
3		27/5	1	20.08	6	1	14.08	AFF NO:301854
4		27/8	0	17.08	-	0	17.08	AFF NO:775012
5		28/1	2	0	2	1	38	ALN(A)(AS)SR:151/2012-13
6		29/3	0	26	1	0	25	ALN(A)(AS)SR:151/2012-13
					TOTAL	8	3	

LAND USE ANALYSIS

SL.NO	DESCRIPTION	AREA IN SQ.M AS PER ZR	%	AREA IN SQ.M AS PER PLAN	%
1	DEVELOPMENT AREA	-	-	2904.43	8.89%
2	ROAD WIDENING AREA	-	-	11307.55	34.60%
3	DRIVE WAY & OPEN AREA	-	-	13066.70	39.99%
4	PARK	3267.79	10%	3,761.23	11.51%
5	CA	1633.90	5%	1,638.00	5.01%
TOTAL				32677.91	100.00%

BUILT UP AREA STATEMENT (TOWER-A + TOWER-B +RECREATIONAL BUILDING + BASEMENT FLOOR)

AREA STATEMENT IN SQM

FLOOR	GROSS AREA	DEDUCTIONS FOR DUCTS & OTS	DEDUCTIONS FOR GARDEN & DOUBLE HT	BUILT UP AREA	NON FAR AREA				TOTAL NON FAR AREA	FAR AREA	NO'S OF UNIT
					PARKING	LIFT	STAIRCASE HEADROOM	REFUGE AREA			
	A	B	B'	C=A-B-B'	D	E	F	F'	G=(D+E+F+F')	H=(C-G)	
BASEMENT - 1	7834.18	28.96	---	7805.22	7500.15	62.94	---	---	7563.09	242.13	---
BASEMENT - 2	7834.18	28.96	---	7805.22	7500.15	62.94	---	---	7563.09	242.13	---
BASEMENT - 3	7834.18	28.96	---	7805.22	7500.15	62.94	---	---	7563.09	242.13	---
GROUND	2904.43	334.01	158.38	2412.04	1022.73	81.12	---	---	1103.85	1308.19	---
1st FLOOR	2816.29	1496.42	341.92	977.95	---	81.12	---	---	81.12	896.83	---
2nd FLOOR	2726.57	163.82	212.40	2350.35	---	81.12	---	---	81.12	2269.23	14
3rd FLOOR	2739.47	163.96	212.40	2363.11	---	81.12	---	---	81.12	2281.99	16
4th FLOOR	2186.52	154.42	---	2032.10	---	62.94	---	---	62.94	1969.16	16
5th FLOOR	2186.52	154.42	---	2032.10	---	62.94	---	---	62.94	1969.16	16
6th FLOOR	2186.52	154.42	---	2032.10	---	62.94	---	---	62.94	1969.16	16
7th FLOOR	2186.52	154.42	---	2032.10	---	62.94	---	---	62.94	1969.16	16
8th FLOOR	2186.52	154.42	---	2032.10	---	62.94	---	---	62.94	1969.16	16
9th FLOOR	2186.52	154.42	---	2032.10	---	62.94	---	---	62.94	1969.16	16
10th FLOOR	2186.52	154.42	---	2032.10	---	62.94	---	---	62.94	1969.16	16
11th FLOOR	2186.52	154.42	---	2032.10	---	62.94	---	---	62.94	1969.16	16
12th FLOOR	2186.52	154.42	---	2032.10	---	62.94	---	---	62.94	1969.16	16
13th FLOOR	2186.52	154.42	---	2032.10	---	62.94	---	---	62.94	1969.16	16
14th FLOOR	2186.52	154.42	---	2032.10	---	62.94	---	---	62.94	1969.16	16
15th FLOOR	2186.52	154.42	---	2032.10	---	62.94	---	---	62.94	1969.16	16
16th FLOOR	2186.52	154.42	---	2032.10	---	62.94	---	---	62.94	1969.16	16
17th FLOOR	2186.52	154.42	---	2032.10	---	62.94	---	---	62.94	1969.16	16
18th FLOOR	2186.52	154.42	---	2032.10	---	62.94	---	---	62.94	1969.16	16
19th FLOOR	2186.52	154.42	---	2032.10	---	62.94	---	---	62.94	1969.16	16
20th FLOOR	2186.52	154.42	---	2032.10	---	62.94	---	331.08	394.02	1638.08	12
21st FLOOR	2186.52	154.42	---	2032.10	---	62.94	---	---	62.94	1969.16	16
22nd FLOOR	2186.52	154.42	---	2032.10	---	62.94	---	---	62.94	1969.16	16
23rd FLOOR	2186.52	154.42	---	2032.10	---	62.94	---	---	62.94	1969.16	16
24th FLOOR	2186.52	154.42	---	2032.10	---	62.94	---	---	62.94	1969.16	16
25th FLOOR	2186.52	154.42	---	2032.10	---	62.94	---	---	62.94	1969.16	16
26th FLOOR	2186.52	154.42	---	2032.10	---	62.94	---	---	62.94	1969.16	16
27th FLOOR	2186.52	154.42	---	2032.10	---	62.94	---	---	62.94	1969.16	16
28th FLOOR	2186.52	154.42	---	2032.10	---	62.94	---	---	62.94	1969.16	16
29th FLOOR	2186.52	154.42	---	2032.10	---	62.94	---	---	62.94	1969.16	16
30th FLOOR	2186.52	154.42	---	2032.10	---	62.94	---	331.08	394.02	1638.08	12
31st FLOOR	2186.52	154.42	---	2032.10	---	62.94	---	---	62.94	1969.16	16
32nd FLOOR	2186.52	154.42	---	2032.10	---	62.94	---	---	62.94	1969.16	16
33rd FLOOR	2186.52	154.42	---	2032.10	---	62.94	---	---	62.94	1969.16	16
34th FLOOR	2186.52	154.42	---	2032.10	---	62.94	---	---	62.94	1969.16	16
35th FLOOR	2186.52	154.42	---	2032.10	---	62.94	---	---	62.94	1969.16	16
TERRACE	311.81	---	---	311.81	---	---	311.81	---	311.81	---	---
TOTAL	104969.75	7186.53	925.10	96858.12	23523.18	2527.38	311.81	662.16	27024.53	69833.59	534

FAR CALCULATIONS :

$$\text{FAR} = \frac{\text{TOTAL FAR AREA}}{\text{SITE AREA - CA}}$$

$$\text{FAR} = \frac{69833.59\ \text{Sqm}}{32677.91\text{-}1638.00\ \text{Sqm}} = 2.249 < 2.25$$

GROUND COVERAGE :

$$\text{COVERAGE} = \frac{\text{GF AREA+SWIMMING POOL}}{\text{SITE AREA-CA-ROAD}} \times 100$$

$$\text{COVERAGE} = \frac{2904.43+598.14}{32677.91\text{-}1638\text{-}11307.55\ \text{Sqm}} = 17.75\% < 55\%$$

TOTAL BUILDING HEIGHT IS = 109.15 m & 14.60 m

NOTE : ALL DIMENSIONS ARE IN METER

SCALE - 1: 400

DWG No : 06 OF 13

DRAWINGS:
GROUND FLOOR PLAN

TITLE :-

PROPOSED RESIDENTIAL APARTMENT PLAN IN SYNO:27/1, 27/3, 27/5, 27/8, 28/1 & 29/3, OF KADA AGRAHARA VILLAGE, SARJAPURA HOBLI, ANEKAL TALUK, BANGALORE DIST.

OWNER:-

Debleena Banerjee

Ms . DEBLEENA BANERJEE

Darshan

Mr . DARSHAN KANNAN

M/s GODREJ PROPERTIES LTD

ENGINEER:-

B. V. P

(PRAVEEN .B. V)
Reg.No: BCC/BL-3.6 / E: 0099/ 2024-25

ಪ್ರಾಧಿಕಾರದ ಪತ್ರ ಸಂಖ್ಯೆ ಆಯೋಪ್ರಾ/188/193
2026-27 ದಿನಾಂಕ 09 JUL 2026
ನಿಬಂಧನೆಗೊಳಪಡಿಸಿ ನಕ್ಷೆ ಅನುಮೋದಿಸಲಗಿದೆ.
ಸದಸ್ಯ-ಕಾರ್ಯದರ್ಶಿ,
ಆನೇಕಲ್ ಯೋಜನಾ ಪ್ರಾಧಿಕಾರ,
ಆನೇಕಲ್.