

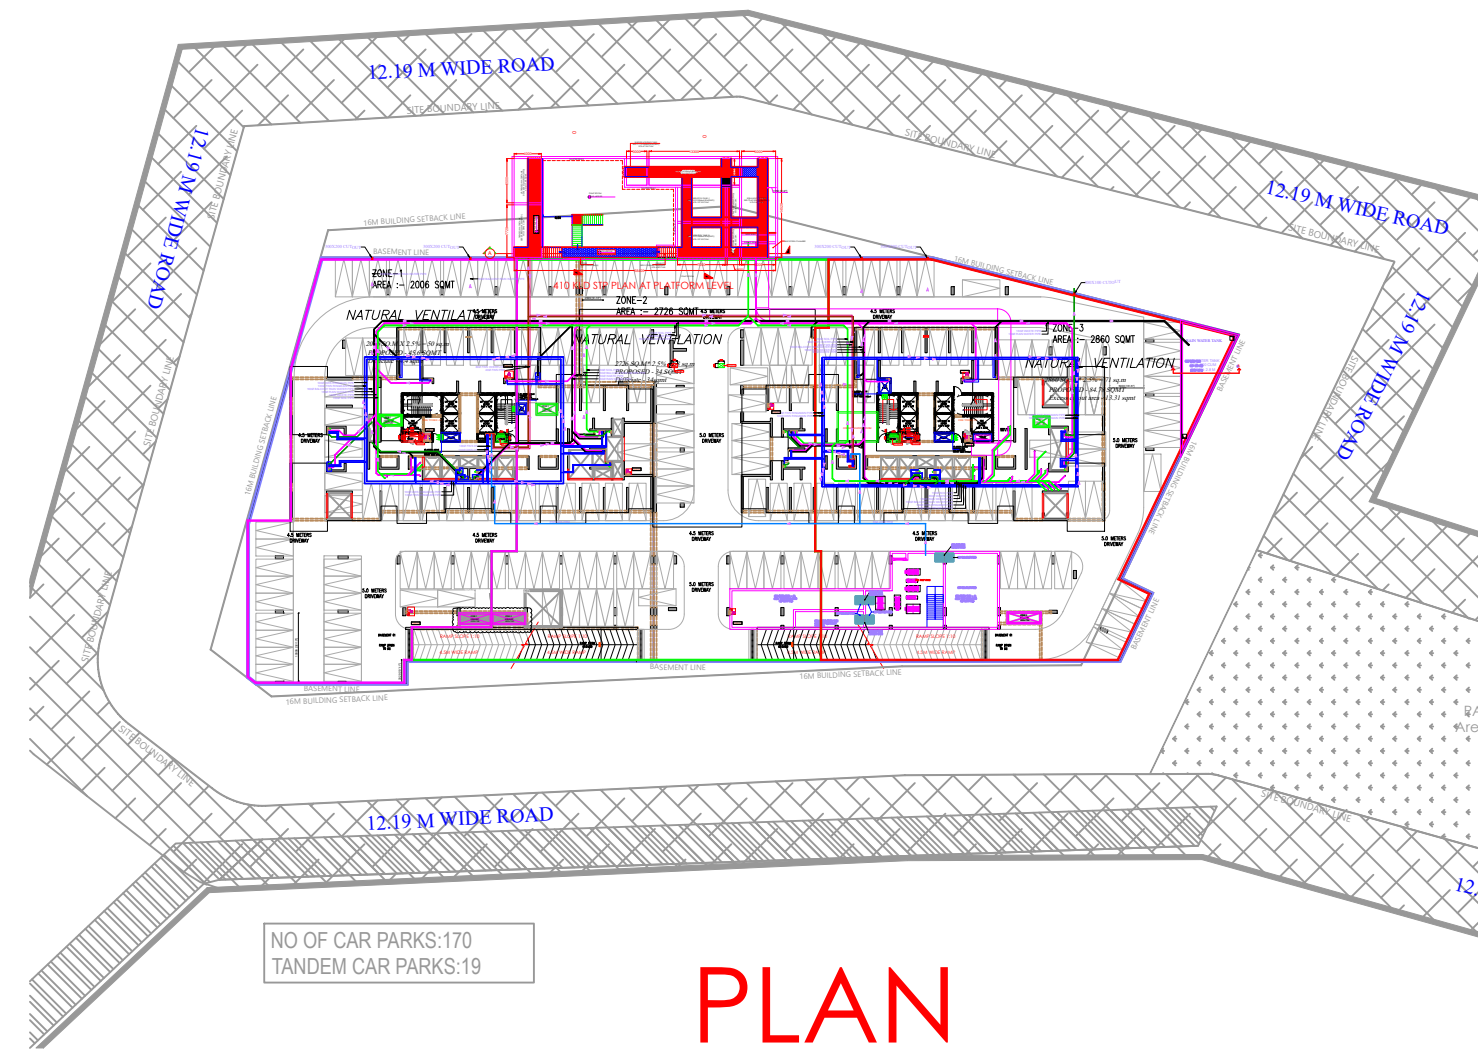


THIS DRAWING IS THE PROPERTY OF CUBEROOT ENGINEERING SERVICE CONSULTANTS.
NO PART OF THE DRAWING MAY BE REPRODUCED IN ANY MANNER WHATSOEVER
WITHOUT WRITTEN PERMISSION FROM CUBEROOT ENGINEERING SERVICE CONSULTANTS.


- NOTES :
1. ALL DIMENSIONS ARE IN MM UNLESS OTHERWISE SPECIFIED.
 2. DO NOT SCALE THE DRAWING REFER TO DIMENSIONS AS INDICATED.
 3. IF ANY DISCREPANCY FOUND CONTRACTOR TO BRING TO THE NOTICE OF THE CONSULTANTS BEFORE EXECUTION.
 4. THIS DRAWING TO BE READ IN CONJUNCTION WITH RELEVANT ARCHITECTURAL, STRUCTURAL AND OTHER SERVICES GFC DRAWINGS.

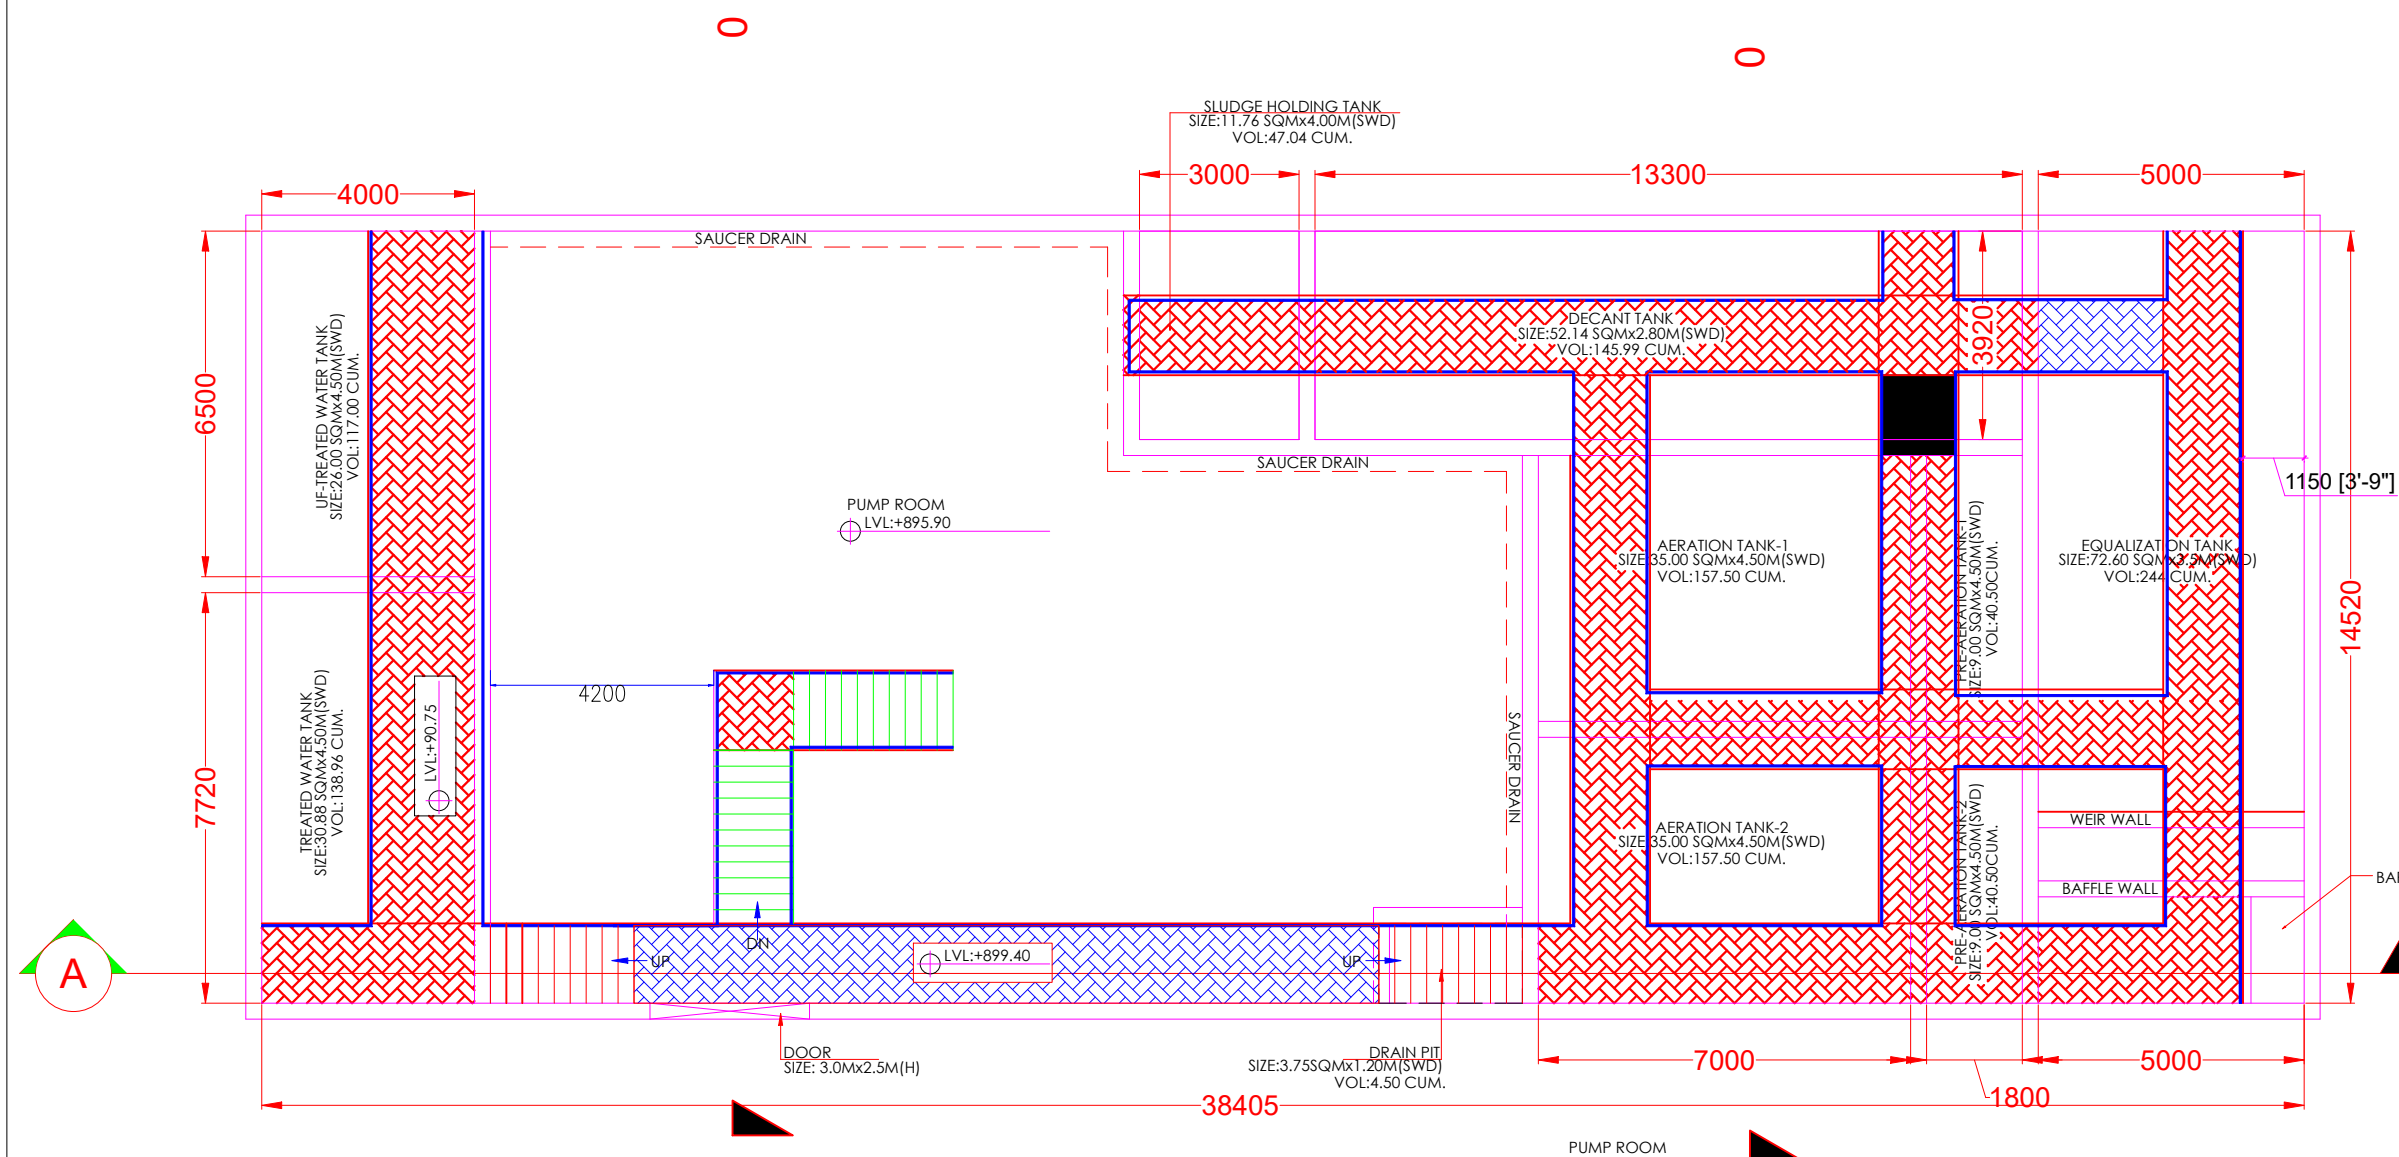

410 KLD STP PLAN AT PLATFORM LEVEL

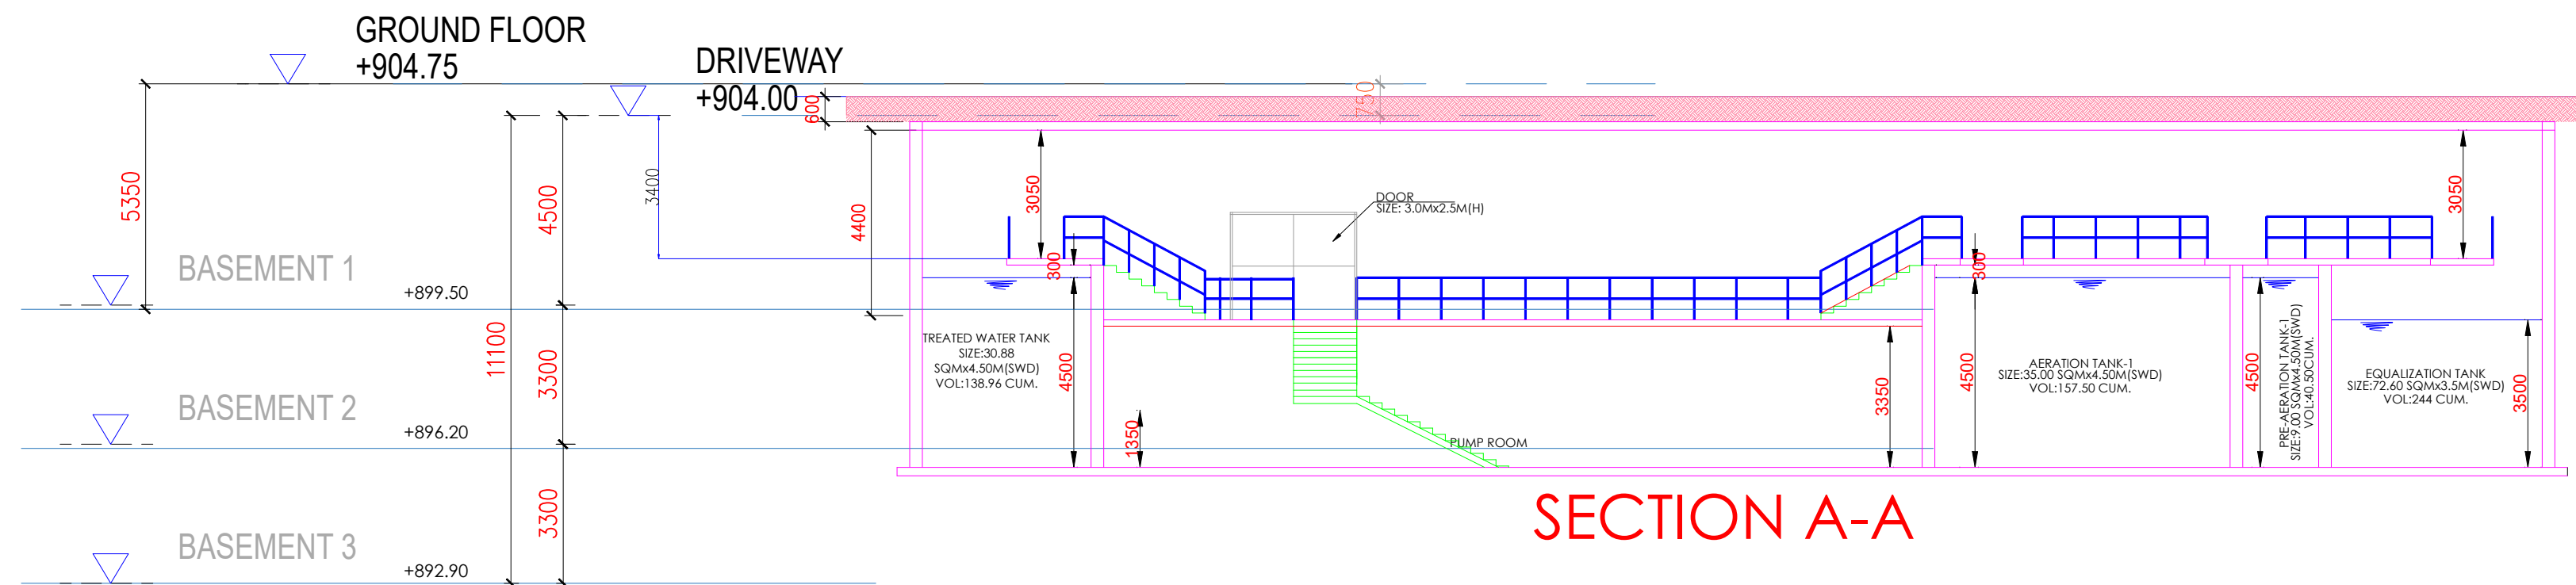

SECTION A-A

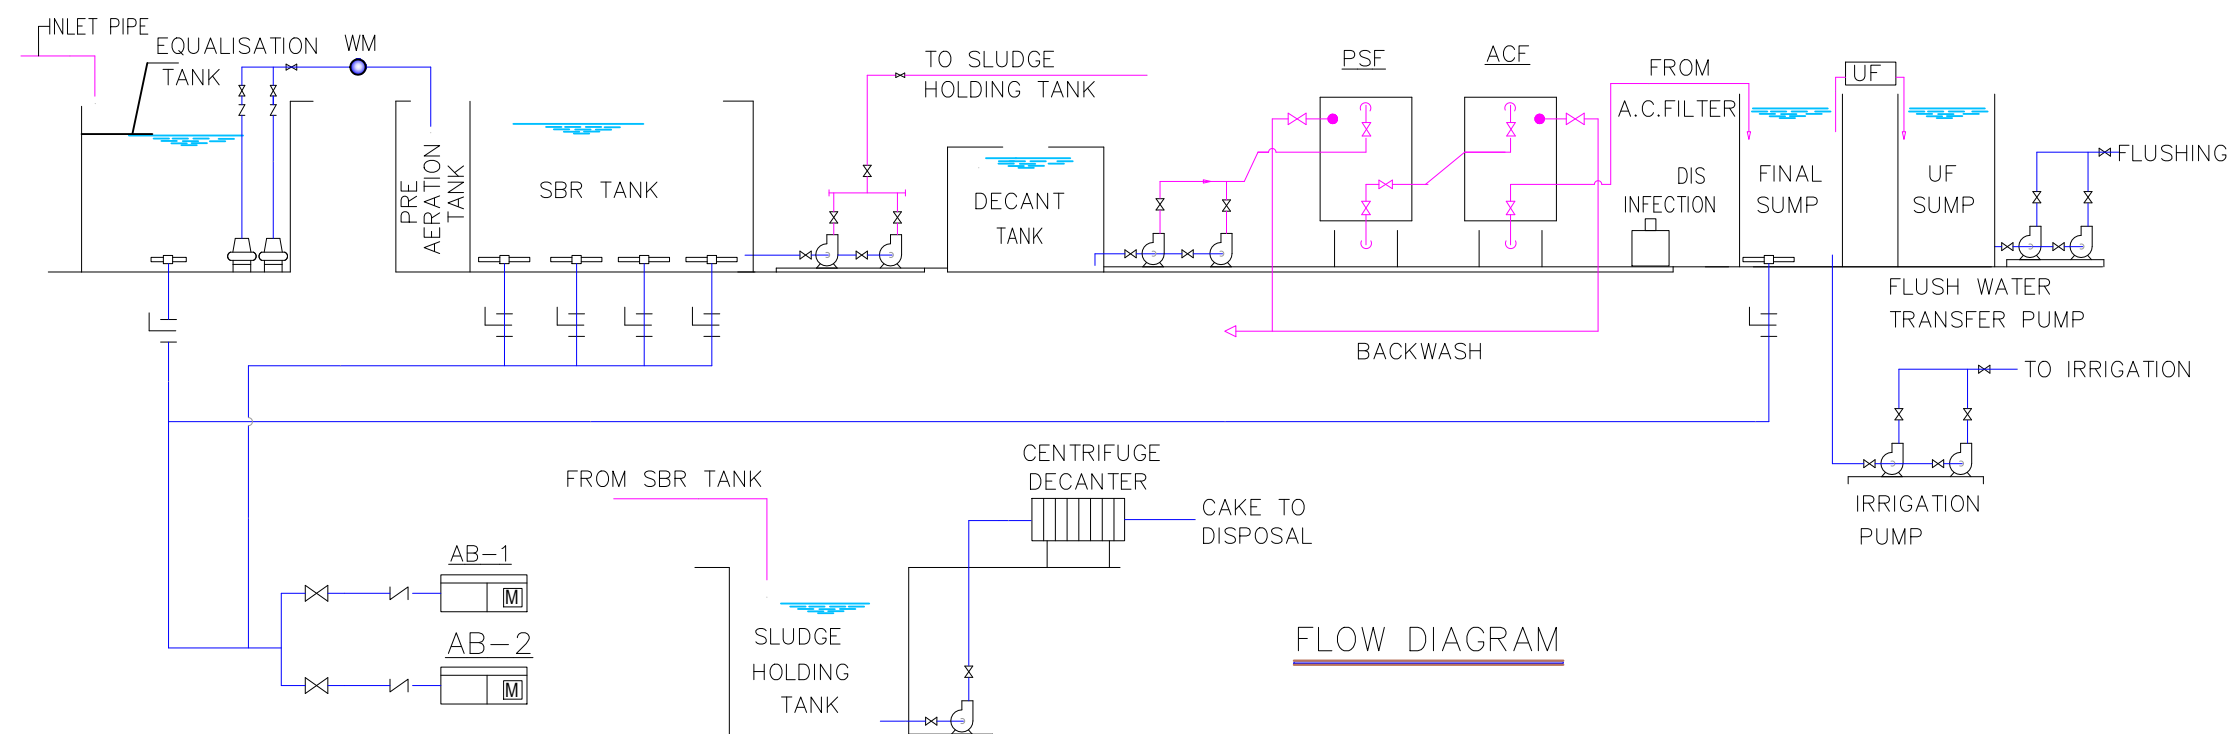

FLOW DIAGRAM

11.02.2025	FOR APPROVAL		
REV	DATE	DESCRIPTION	DRAWN / APP.
		REVISION	

PROJECT TITLE :
PROPOSED TOWNSHIP DEVELOPMENT
AT KADAAGRAHARA, BANGALORE

CLIENTS :
M/S GODREJ PROPERTIES

ARCHITECT:
DP ARCHITECTS PTE LTD
6 RAFFLES BOULEVARD
#04-100 MARINA SQUARE
SINGAPORE 039594
TEL 63383988 FAX 63379989

CONSULTANT'S SIGNATURE


MEP CONSULTANTS :
CUBEROOT ENGINEERING SERVICE CONSULTANTS LLP
 # 771, 3rd floor, 5th main,
Bikaspur, 560 075,
Bengaluru - 560 075
Mob - 98753 46187
Email - info@cuberootconsultants.com

SANCTION LAYOUT
DRAWING TITLE :
410 KLD STP PLAN &
SECTION DETAILS

FILE NAME:		
DRAWN : CSR	DATE : 10.07.2026	REV
DESIGNED : ANUJ	SCALE : 1:100	R0
CHECKED : PRASAD	SHEET : 1 OF 1	
JOB No : CR-116	DRAWING No : CR-GK-PL-115	